


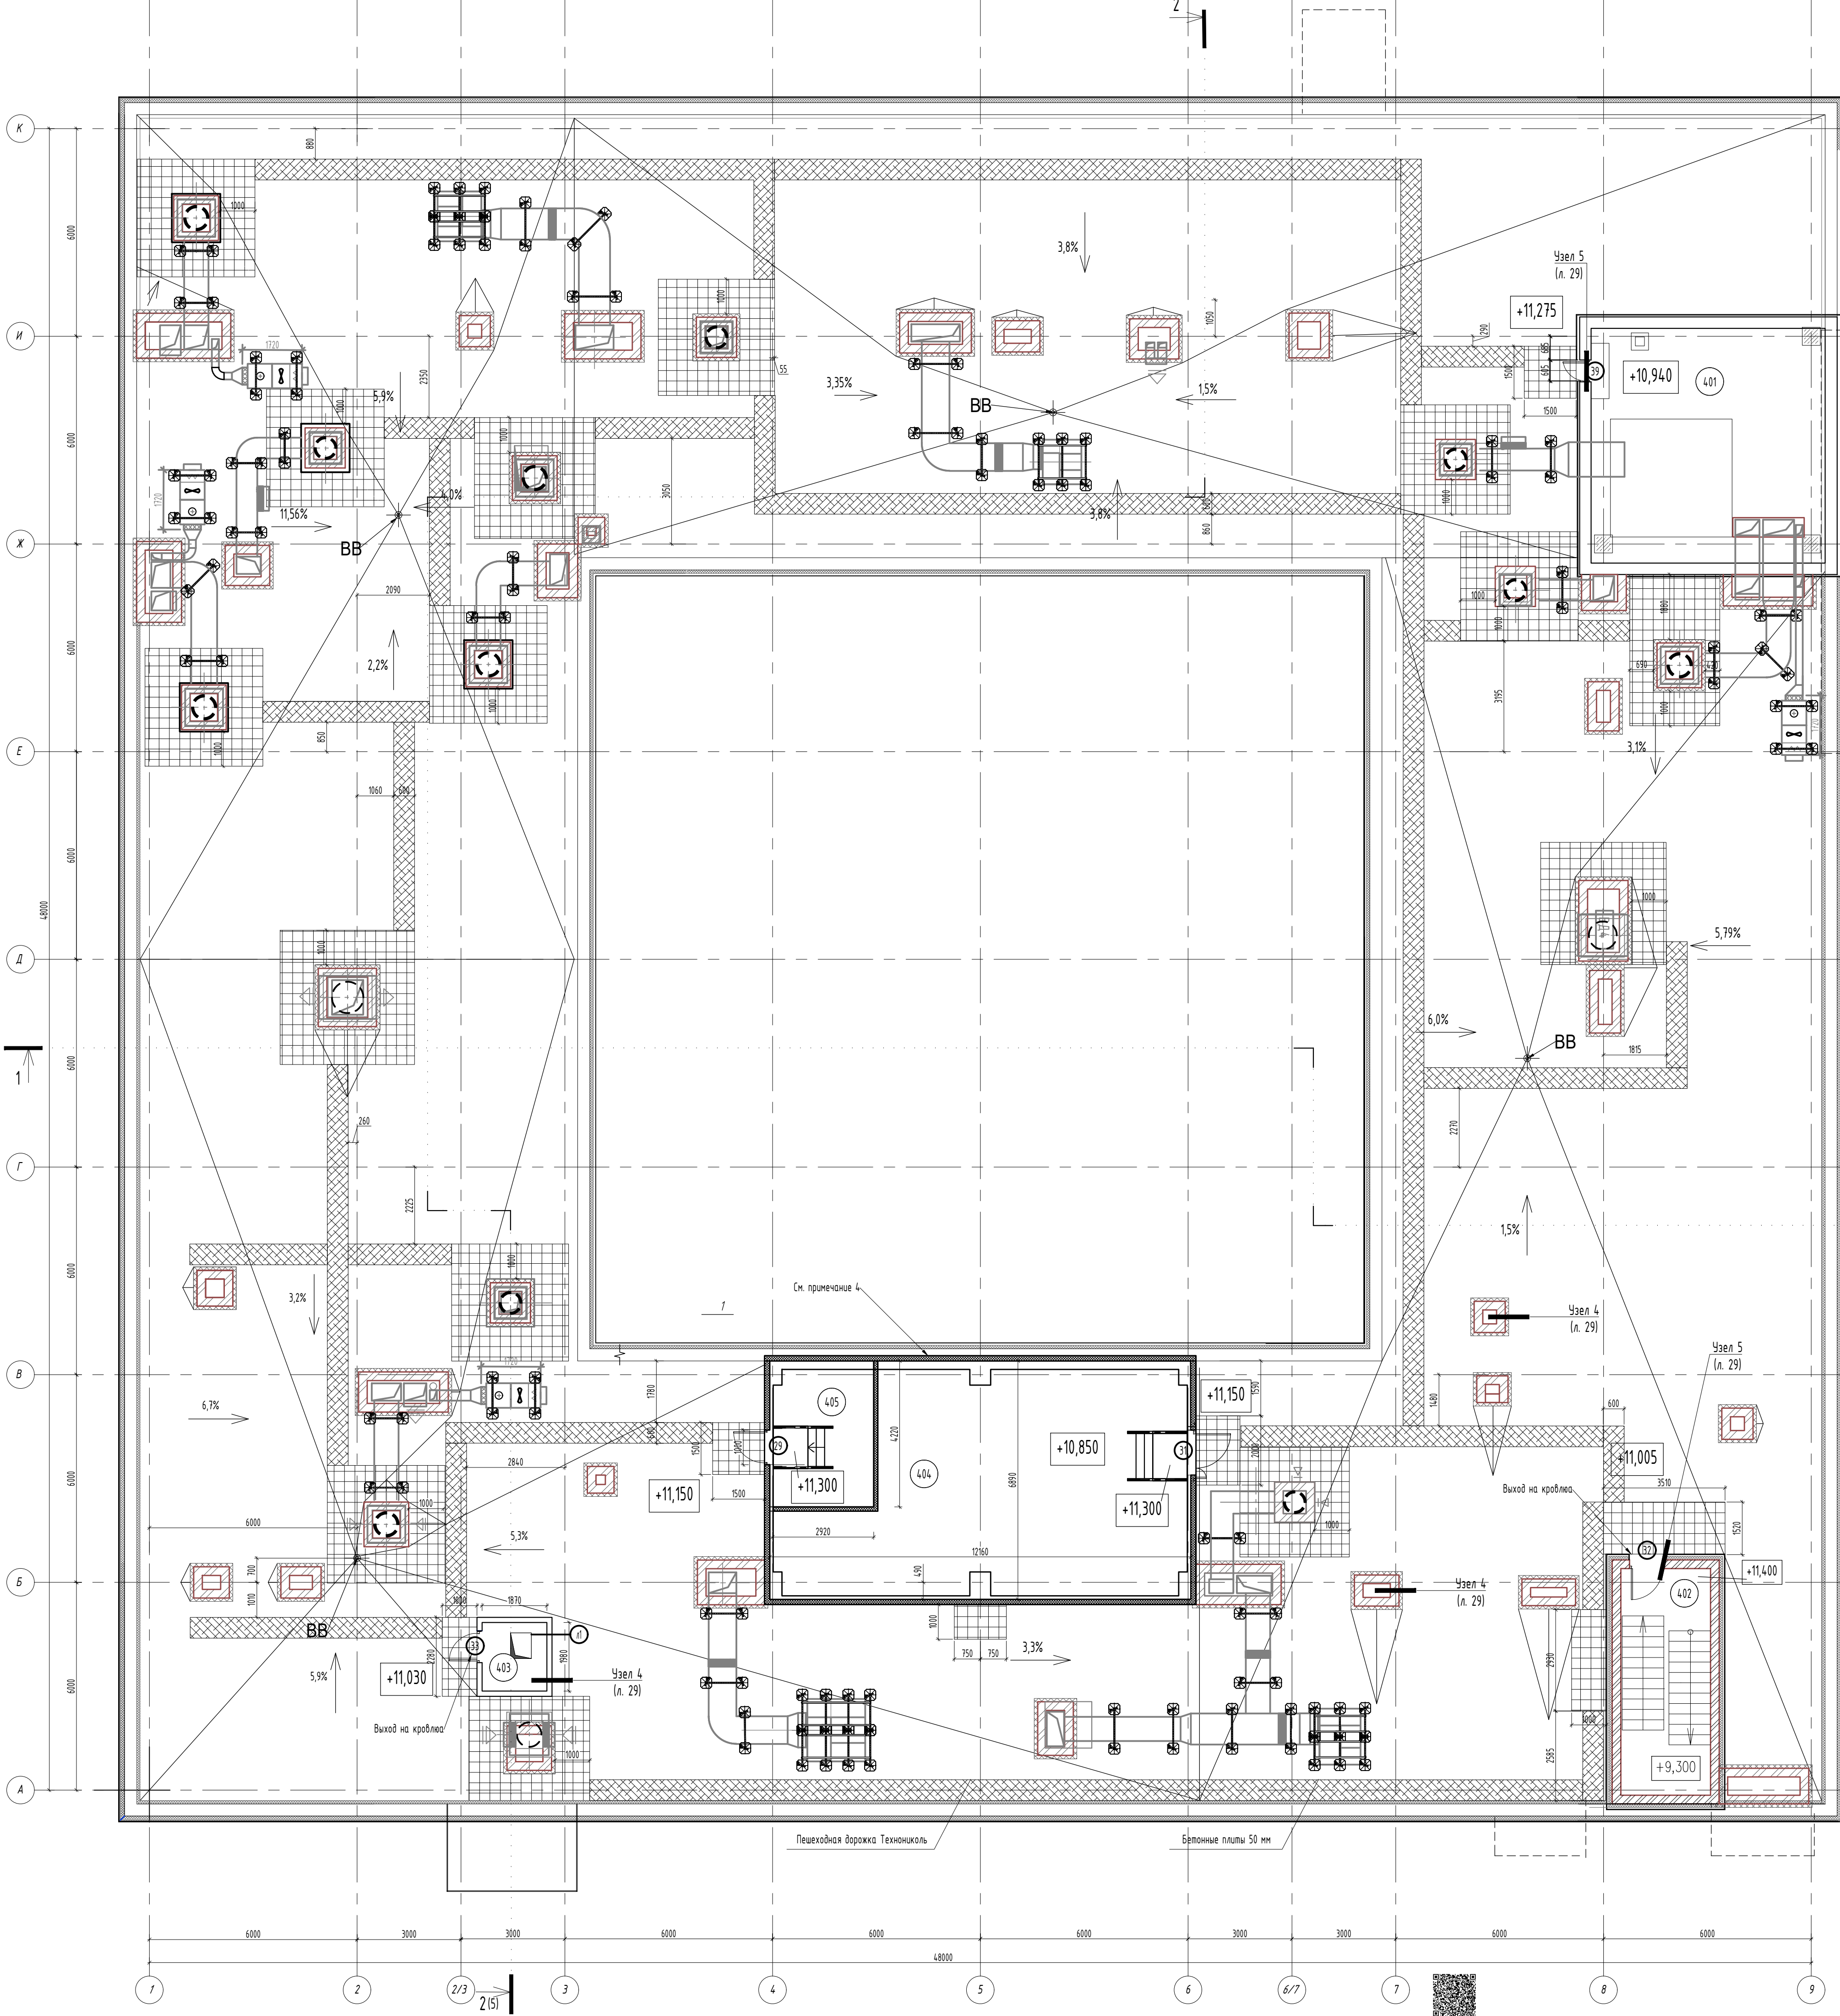

Экспликация помещений			
Номер пом.	Наименование помещения	Площадь, м²	Кол. пом.
401	Техническое помещение	44,46	
402	Выход на крыло 1	16,87	
403	Выход на крыло 2	3,70	
404	Венткамера	65,44	
405	Техническое помещение	11,76	
Итого		142,23	

Условные обозначения:



- протекторная плитка толщиной не менее 40мм на скрытых несущих опорах
- Пешеходная дорожка для битумных кровель ТехноНИКОЛЬ шириной 600мм

Условные обозначения:

- Существующие стены - кирпич, толщиной 510 мм
- Монтаж перегородок из кирпича, толщиной 120 мм
- Монтаж перегородок из ГКЛ, толщиной 125 мм
- Номер помещения
- Лопат в полу для инженерных коммуникаций
- Марка двери

- Конструкция шахт на крыше см. в разделе АС2 и совместно с разделом ОБ
- Узлы кровли см. на листе 29
- Спецификация водостока см. на листе 30
- Раскладку знаков-панелей для устройства венткамеры см. на листе 17, конструкция помещения венткамеры см. в разделе АС2

						01-2024/ИВН-АР			
						«Забережение строительства административно-лабораторного корпуса - здание 24, входящего в состав объекта Масковская мебельная фабрика (комплекс научных сооружений ИВН), расположенного по адресу: г. Москва, г. Троицк, ул. Физическая, 27»			
Изм.	Колуч.	Лист	№ док.	Подп.	Дата	Административно-лабораторный корпус здание 24	Стация	Лист	Листов
Разработ.		Свечникова					Р	8	
Проверил									
ГИП		Фидорко							
План на отм. +0,050							000 "ЕСК"		

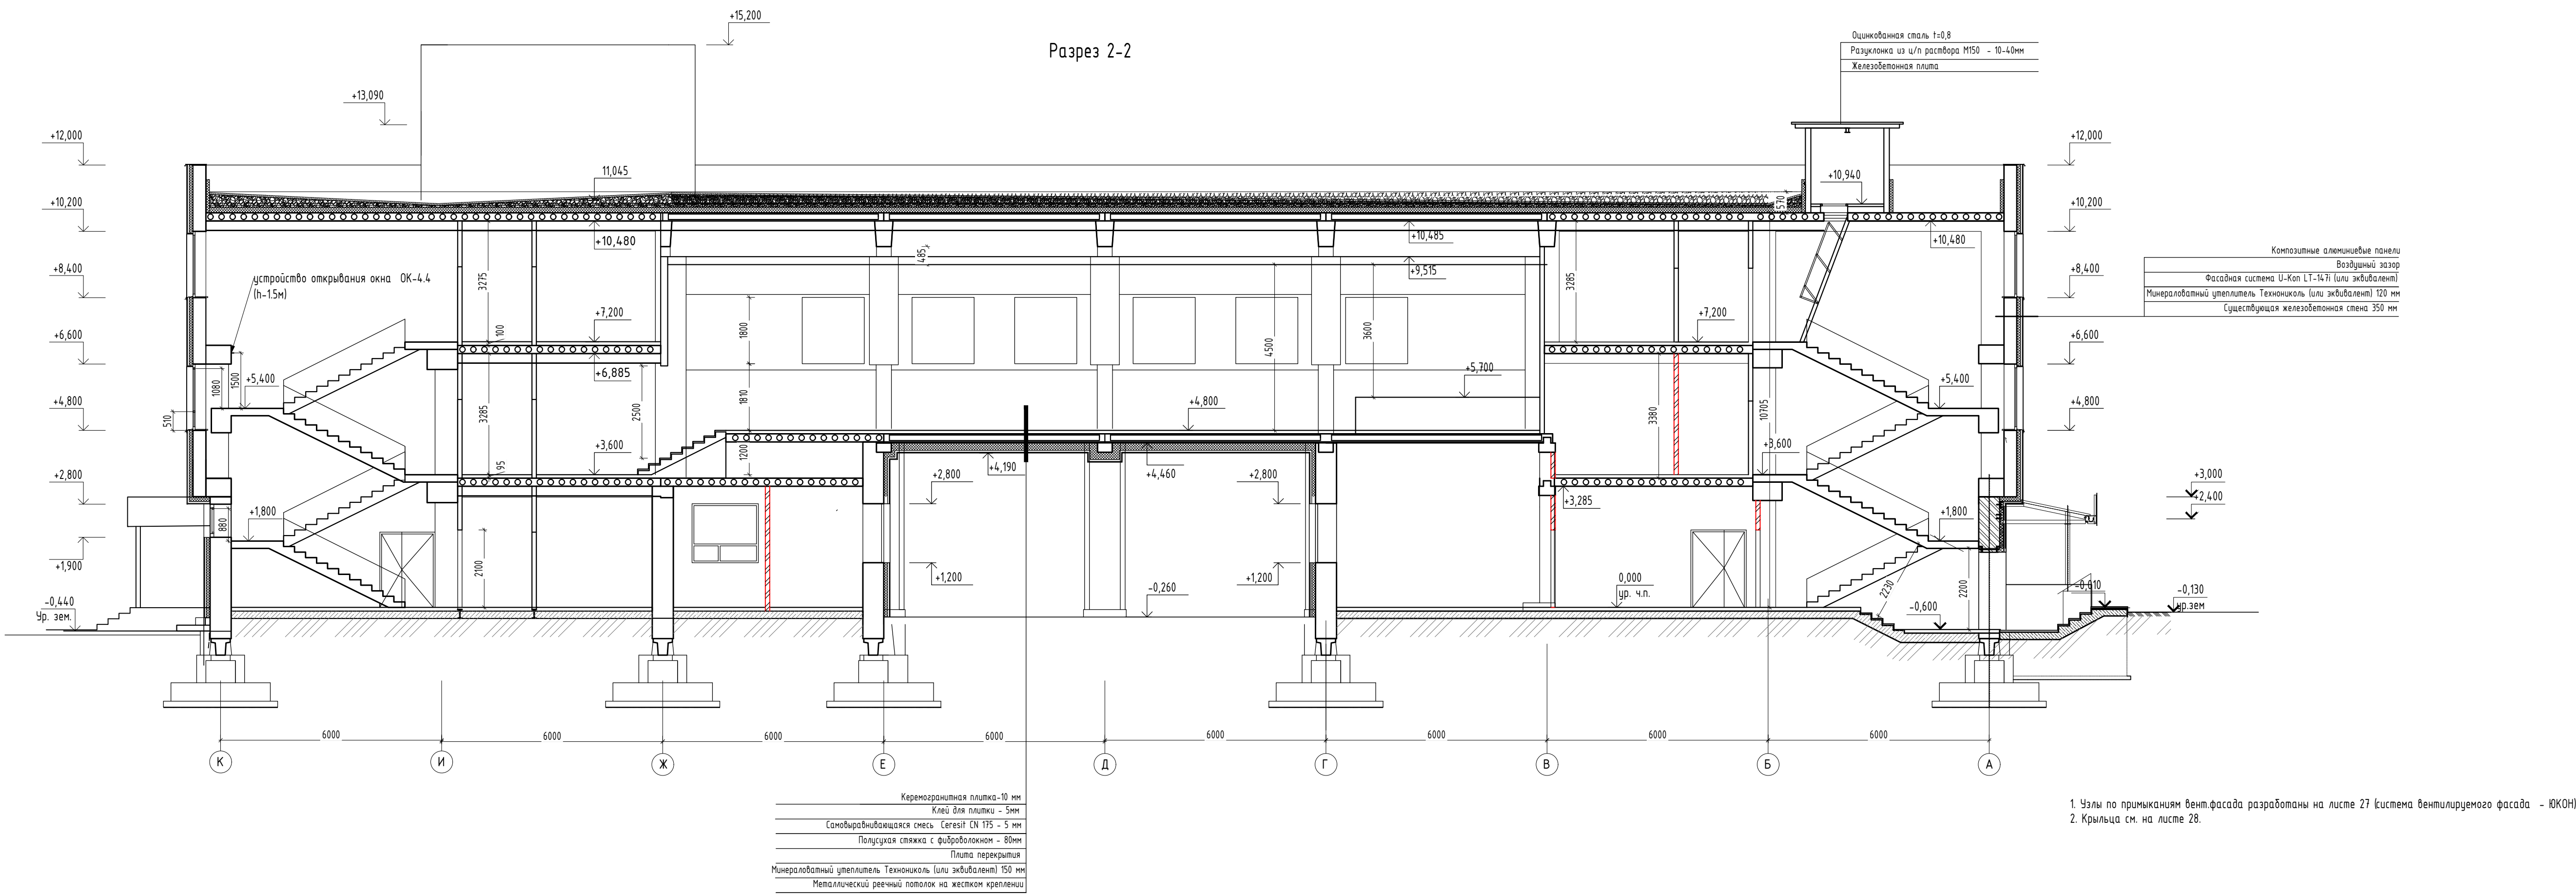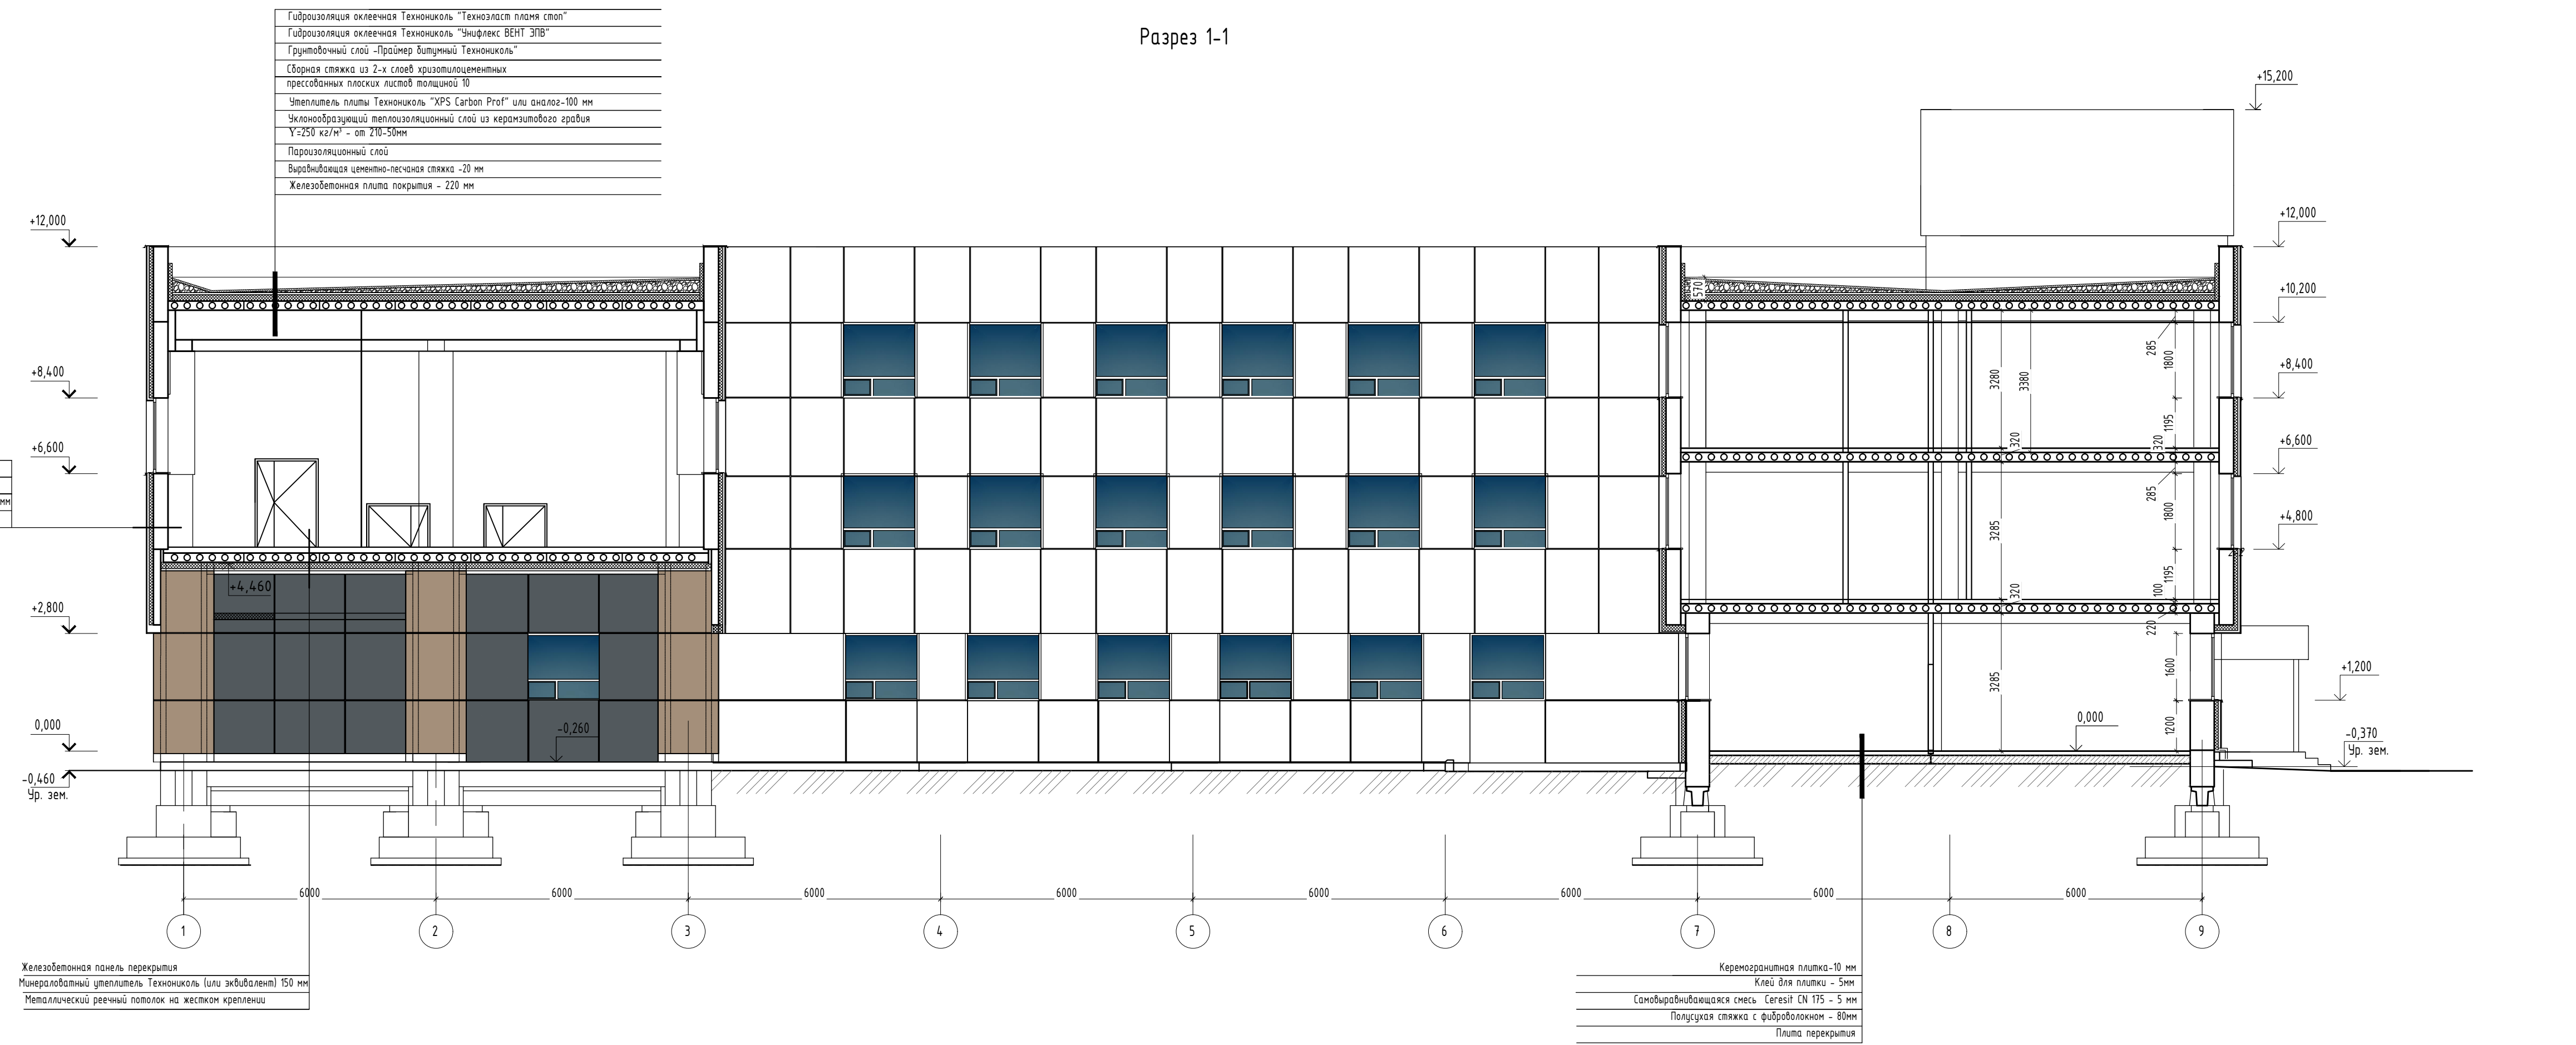

						01-2024/ИВН-АР			
						«Завершение строительства административно-лабораторного корпуса - здание 24, входящего в состав объекта Московской негосударственной фабрики (комплекс научных сооружений) ИВН, расположенного по адресу: г. Москва, г. Троицк, ул. Физическая, 27»			
Изм.	Жолуч	Лист	№ док	Подп.	Дата	Административно-лабораторный корпус здание 24	Стадия	Лист	Листов
Разраб.	Свечникова						Р	10	
Проверил									
ГИП	Фидирко					Разрез 1-1, 2-2	000 "ЕСК"		